

PROYECTO:

**CONSTRUCCIÓN DE
VIVIENDA
UNIFAMILIAR**

PROPIETARIO:

**CONSULTORIA Y
CONSTRUCCIONES
ARQUITUDIO S.A**

observación:

todas las medidas anotadas en este plano debe ser verificadas por el constructor de la obra cualquier cambio a lo planificado debera ser aprobado por el proyectista

es obligatorio que el constructor entregue copias en el que consten todos los cambios

CONTIENE:

**IMPLANTACION
INSTALACIONES SANITARIAS
SIMBOLOGIA**

Diseño sanitario:

Ing. Danyra Cavallero Contral
REG. PROF. No. 1016-2022-258758

Responsabilidad tecnica:

ARQ. JAMAR DELGADO BELLO
REG. PROF. No. 1016-10-98211

Fecha:

MARZO 2026



Lámina:

E6

Escala:

Indicadas

Espacio para sellos:

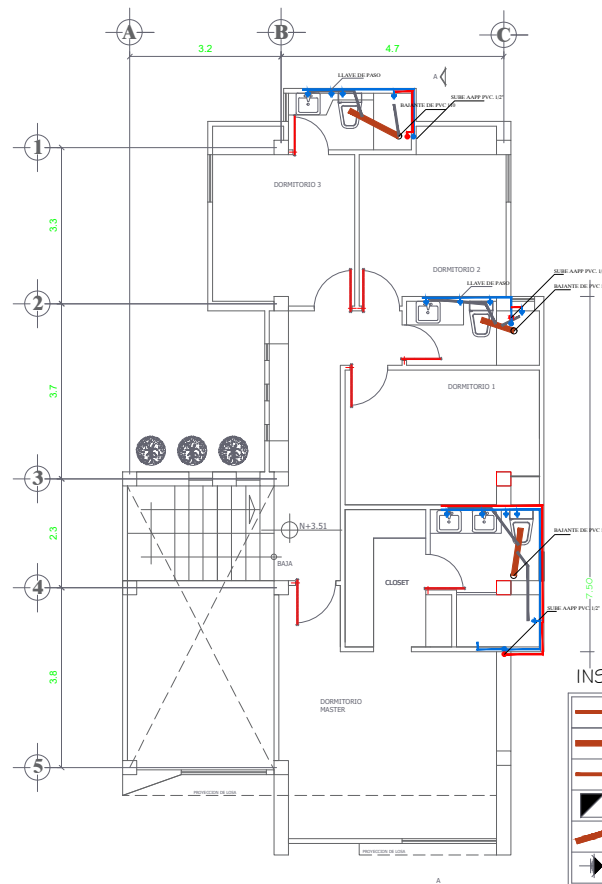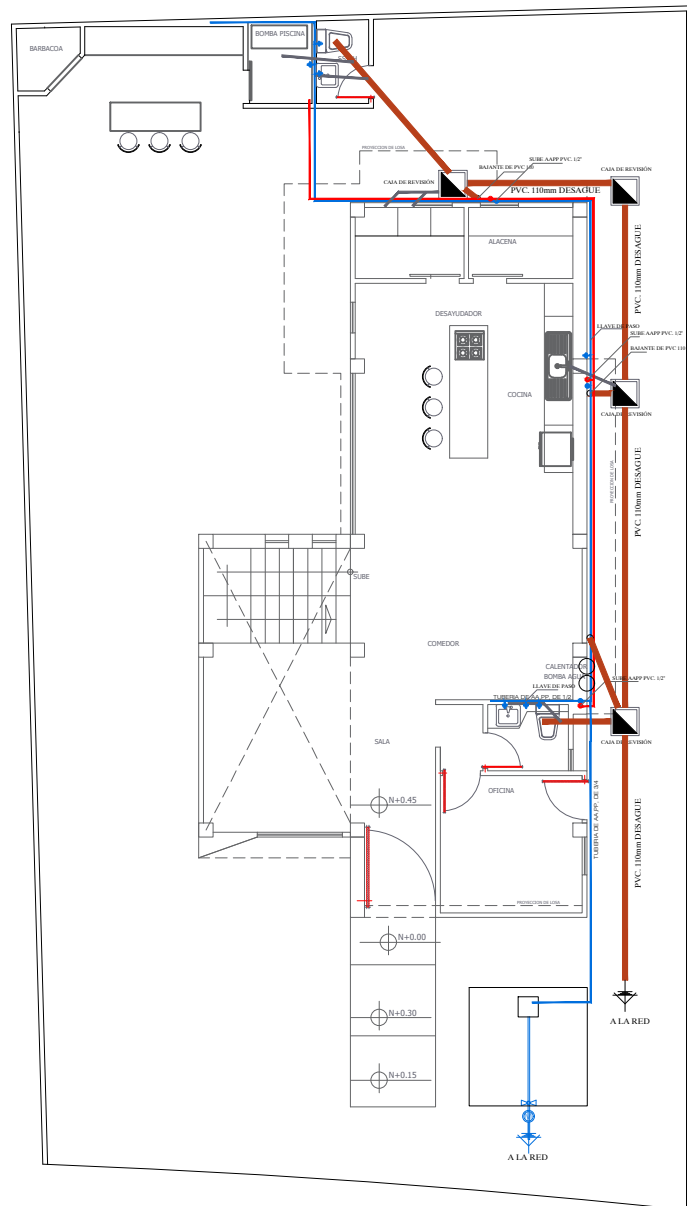

INSTALACIONES SANITARIAS AAPP Y AASS
ESCALA: 1:75
PLANTA ALTA

INST. AGUAS SERVIDAS

	SUMIDERO DE PISO
	TUBERIA P.V.C. 110mm
	TUBERIA P.V.C. 55mm.
	CAJA DE REVISION.
	BAJANTE DE AA.SS.
	ACOMETIDA A LA RED.

INST. DE AGUA POTABLE

	TOMA DE AA.PP.
	MEDIDOR.
	LLAVE CHECK.
	ACOM.PRINCIPAL AAPP.
	BOMBA DE AGUA.
	COLUMNA DE AAPP. BAJANTE
	TUBERIA AAPP.